
PRUEBA DE CONCEPTO · PROOF OF CONCEPT

Ejemplo del formato y nivel de acabado exigido al entregable A-101.
Geometría inventada; no resuelve ninguna cuestión del registro de decisiones.

PLANTA BAJA · cota ±0,00 · escala 1:100

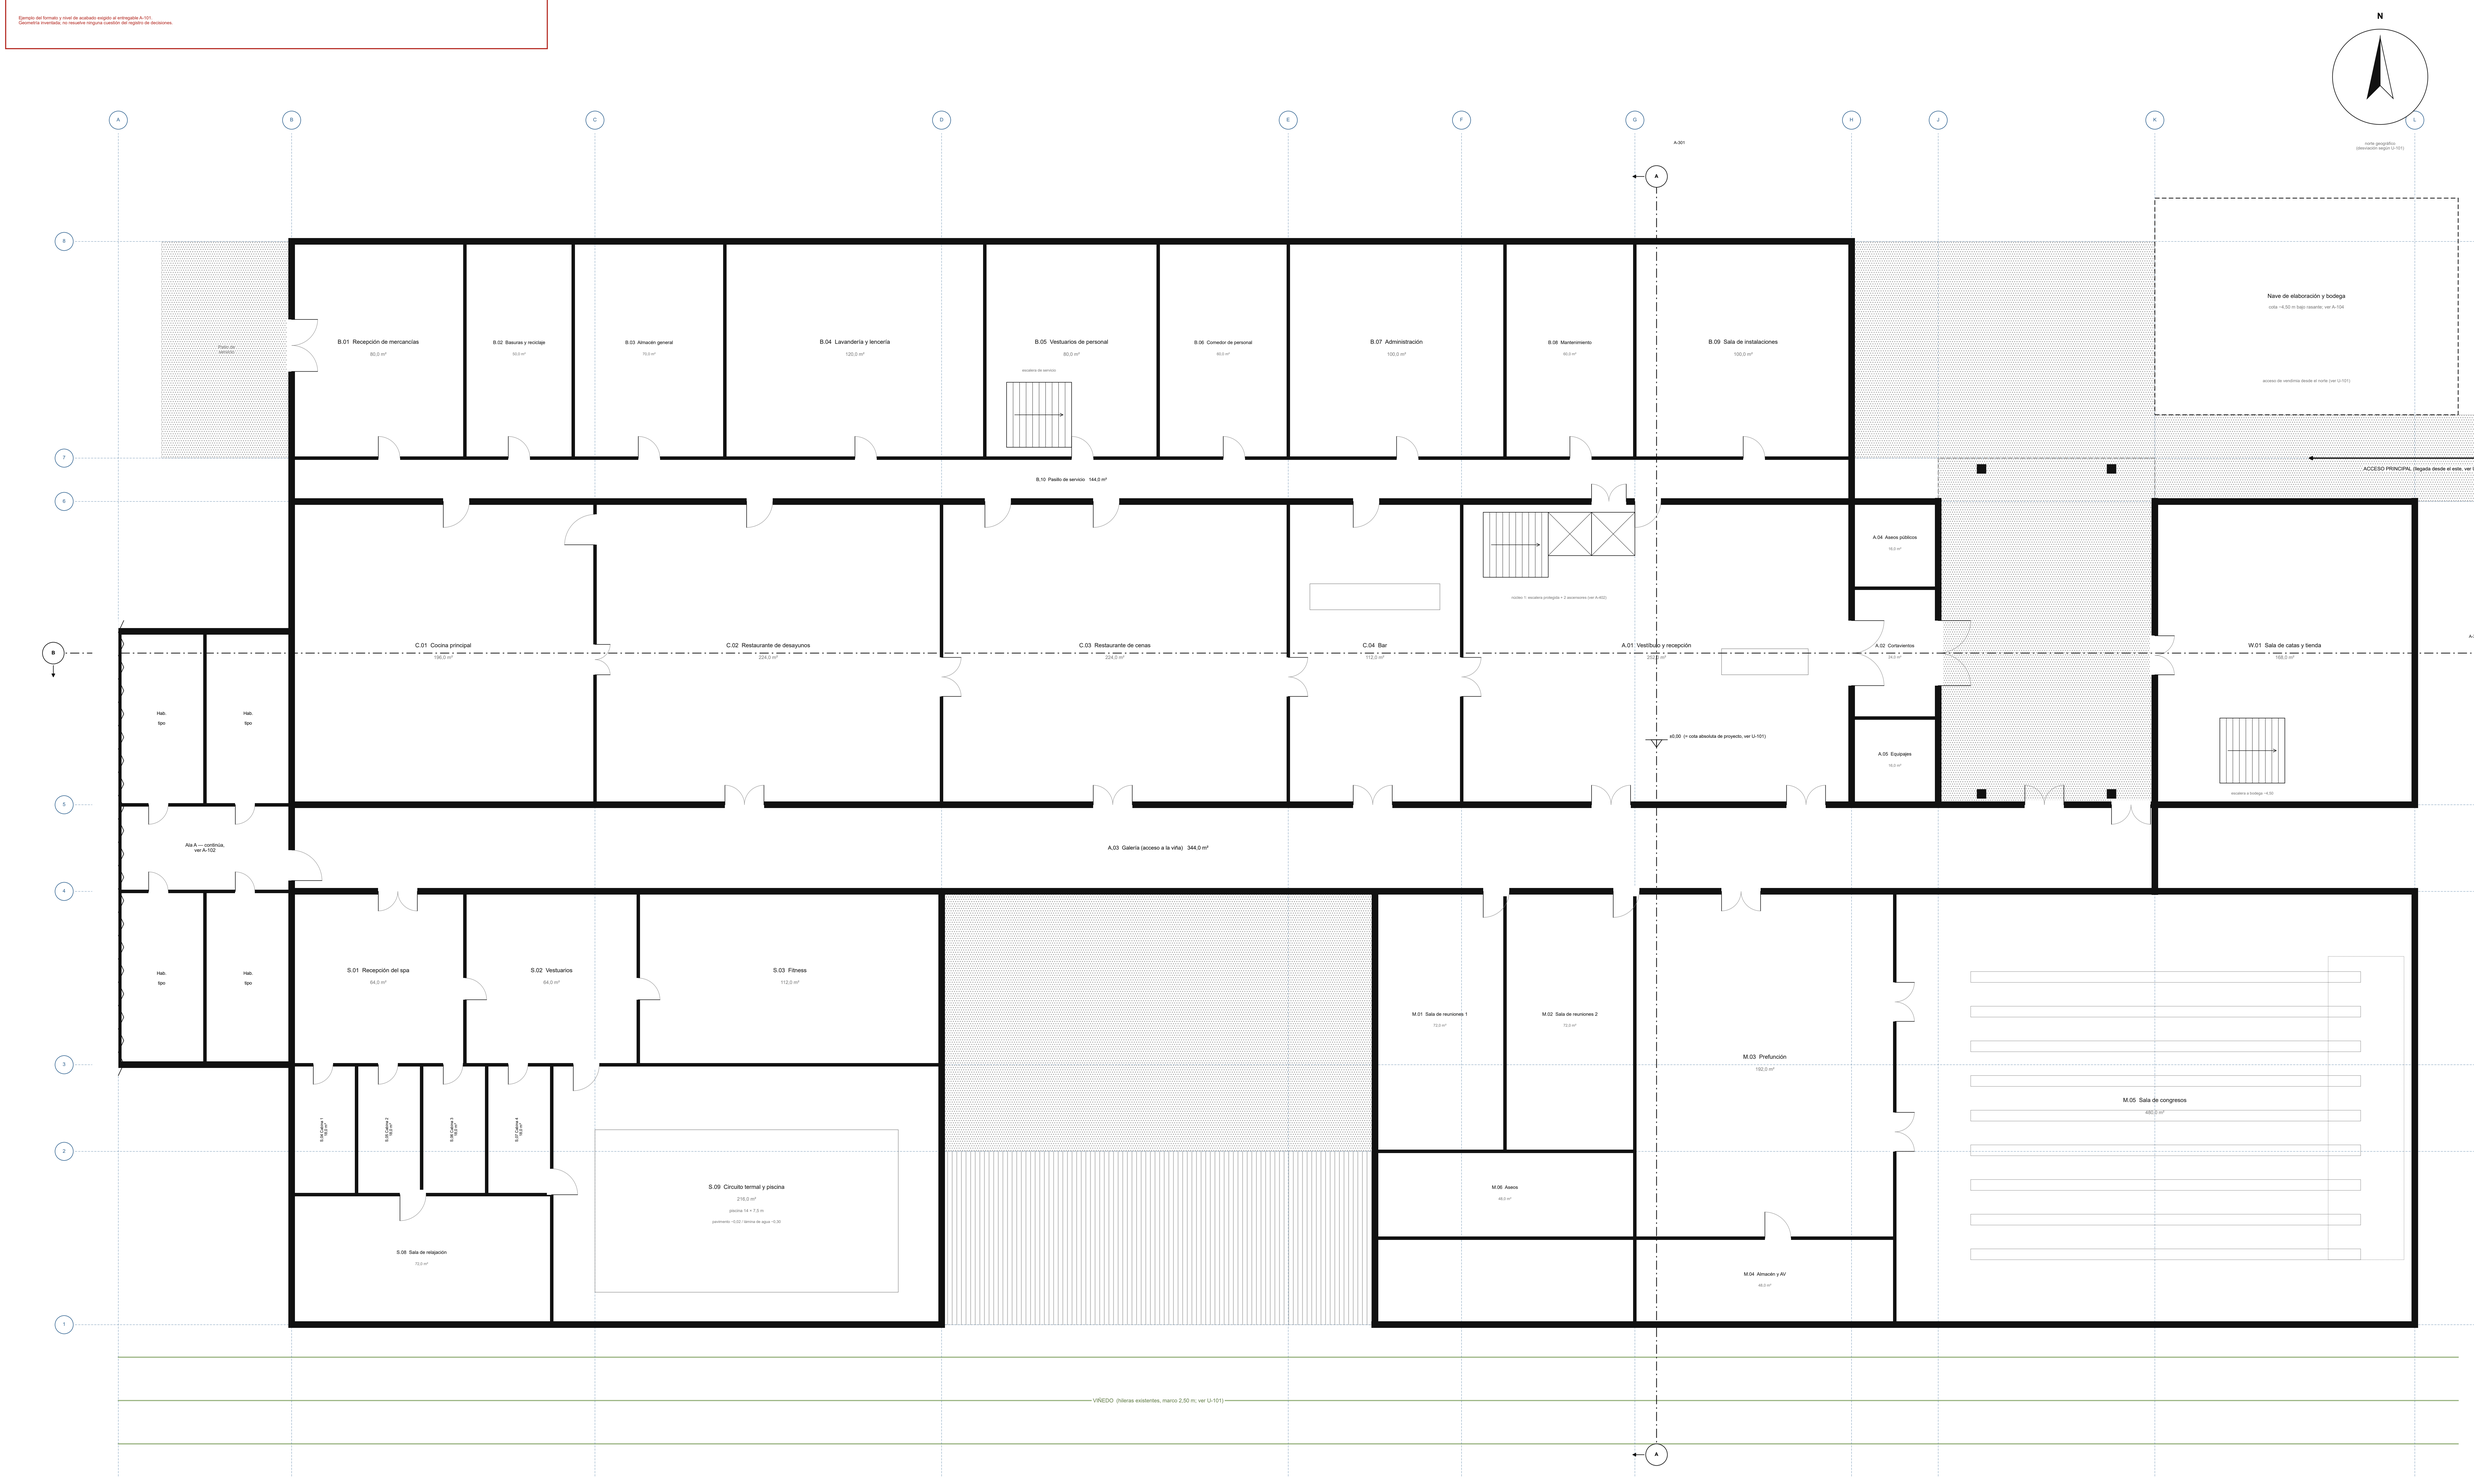

ESCALA GRÁFICA 1:100

0 2 4 6 8 10 m

LEYENDA

- muro de fachada / sectorización, e = 300 mm
- tabiquería interior, e = 150 mm
- carpintería acristalada (muro cortina), montantes c/ 1,50 m
- puerta, con sentido de apertura
- volumen fuera de este plano (trazo); ver plano indicado
- eje estructural y referencia de pilar
- pavimento exterior / hileras de viña existentes

SUPERFICIES ÚTILES DE ESTE PLANO (planta baja, m²; medición sobre el dibujo)

Llegada y galería	652,0
Restauración (dos restaurantes, bar, cocina)	736,0
Congresos	912,0
Spa	600,0
Bodega, parte visitable	168,0
Zonas de servicio	864,0
Total superficie útil, planta baja (sin ala de habitaciones)	**3931,0**

Superficie construida y cuadro completo por niveles: A-001. Esta tabla no sustituye a 03-programa/áreas-schedule.csv.

NOTAS GENERALES

1. Cotas en metros; espesores en milímetros. Nivel ±0,00 referido a la cota absoluta fijada en U-101.
2. Superficies útiles medidas según el reglamento turístico de Castilla y León; construidos según ordenanza municipal (ver STANDARDS.md).
3. Sectores de incendio, recorridos de evacuación y ocupación según CTE DB-SI; planos A-002. Itinerarios accesibles DB-SUA 9; A-002.
4. Planta tipo de habitaciones: A-102. Planta de bodega (−4,50) A-104. Secciones A-A y B-B: A-301. Alzados: A-201.
5. Este plano forma parte de proof-of-concept y es un EJEMPLO de formato y nivel de acabado. No representa el proyecto.

Curso de Proyectos — Universidad (ejemplo docente) Propietario / cliente	PLANTA BAJA Superficies útiles, ejes y referencias Título del plano	Proyecto básico Fase (LOE / CTE Anejo I)	sesión PoC Dibujado	1:100 Escala (UNE-EN ISO 5455)	P01 Revisión	ejemplo
Hotel resort en viñedo, 150 llaves Provincia de Soria, Castilla y León Proyecto		EJEMPLO — PRUEBA DE CONCEPTO Estado del documento	— Comprobado — Aprobado	A0 · 2026-10-24 Formato / fecha	m / mm Unidades	A-101 nº de plano